
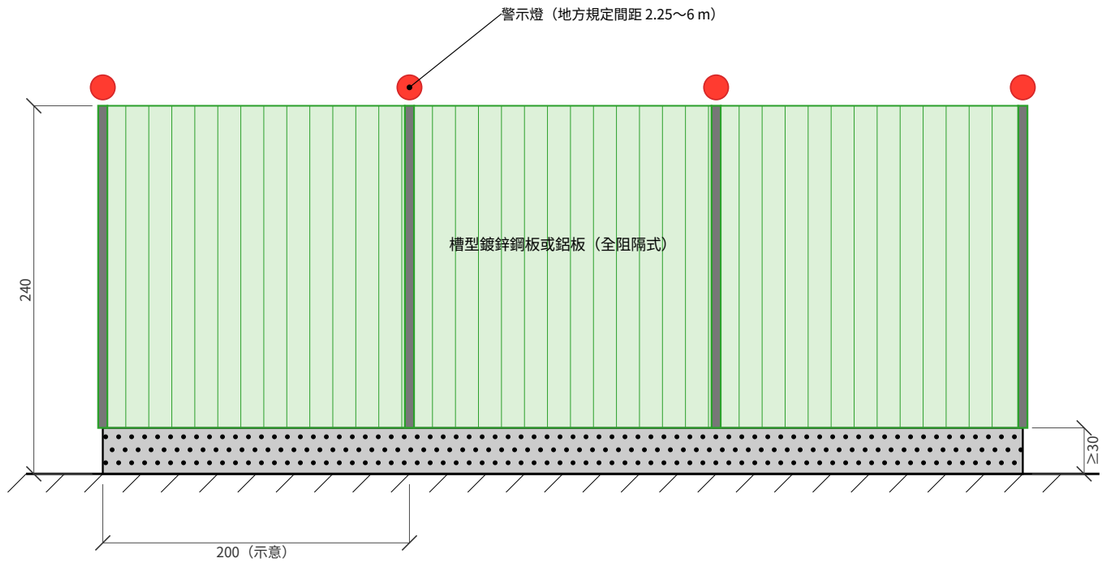


立面圖

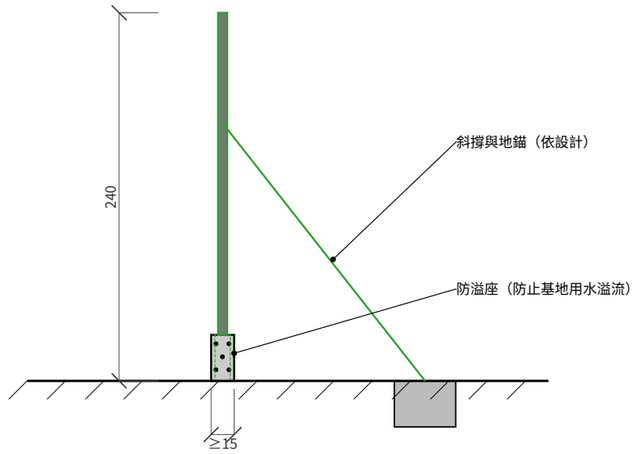

斷面圖

0　0.5　1　1.5　2 m

（工程名稱）

D01 施工圍籬構造詳圖

圖號：D01　比例：1:40（A3）

日期：2026-11-08　單位：公分（另註者除外）

附註

1. 圍籬高度 2.4 m：空污辦法 第6條、附表二【已核】（未提供分級，以第一級繪製）
2. 道路轉角或轉彎處 10 m 內得設半阻隔式（離地 80 cm 以上網狀）：空污辦法 第6條第1項但書【已核】
3. 圍籬定著地面並設防溢座：空污辦法 第6條、附表二【已核】
4. 防溢座 30×15 cm：北市方案 二(三)【地方】
5. 面板厚 1.2 mm 以上：綱要規範 01564 2.2.2（桃園市版）／北市方案 二(二)【地方】
6. 警示燈間距 2.25～6 m：北市方案 二(八)【地方】
7. 立柱間距、埋入深度、斜撐與地錨依設計（示意值非法規值），抗風能力由設計者檢核。
8. 工作場所周圍設固定式圍籬並設警告標示：營造標準 第8條【已核】

【已核】網路條文核對 【待核】使用者核對
【地方】地方規定 【示意】非法規值、依設計


審查


校核

繪圖

設計

施工大門 立面圖（雙扇滑輪平開）

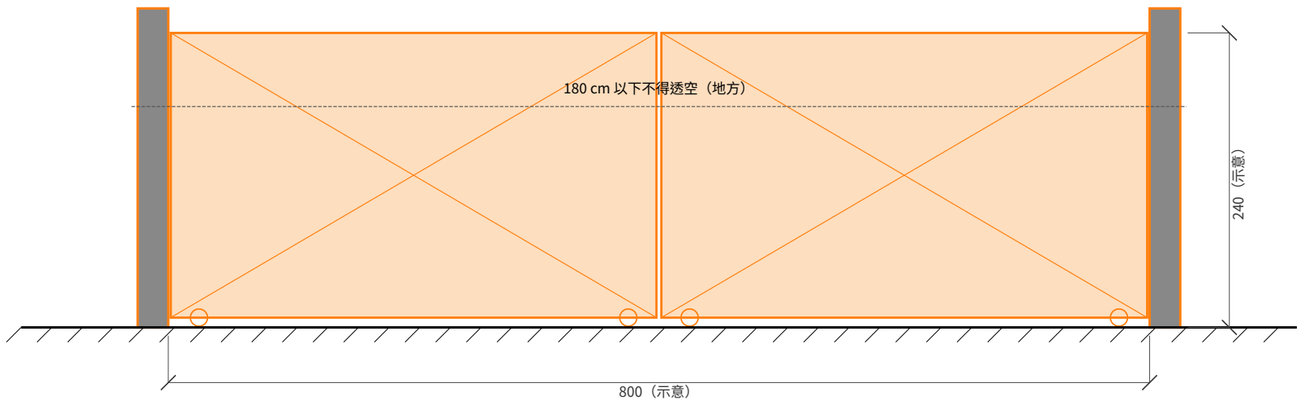

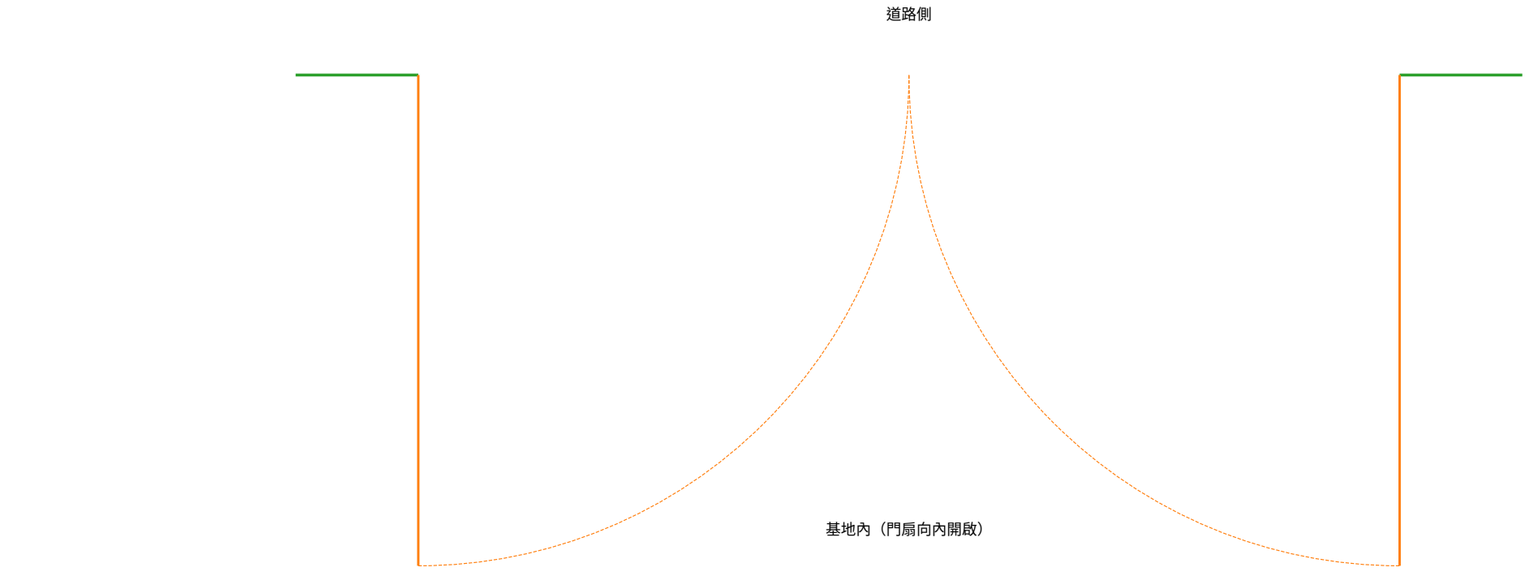

平面圖

（工程名稱）

D02 施工大門構造詳圖

圖號：D02　比例：1:50（A3）

日期：2026-11-08　單位：公分（另註者除外）

附註

1. 門寬依最大進出車輛與轉彎軌跡決定（示意 8 m，依設計）。
2. 門高同圍籬高度；180 cm 以下不得透空、鐵門厚 1.2 mm 以上：北市方案 二(四)【地方】
3. 除車輛出入外隨時關閉；門扇向基地內開啟，不得占用道路。
4. 車輛出入口設交通號誌、標示或柵欄；不足時置交通引導人員：設施規則 第21條之1、第21條之2【已核】
5. 大門處設警示燈與照明；門柱基礎依設計。

【已核】網路條文核對 【待核】使用者核對
【地方】地方規定 【示意】非法規值、依設計

審查	
校核	
繪圖	
設計	

（工程名稱）

D03 洗車台及沉砂池詳圖


圖號：D03　比例：1:100（A3）


日期：2026-11-08　單位：公分（另註者除外）

附註

1. 洗車台四周設防溢座、廢水收集坑及具沉砂作用之沉砂池：空污辦法 第10條【已核】
2. 車輛離場須清洗車體及輪胎，不得附著污泥或造成路面色差。
3. 非區域開發／疏濬工程者，平台長寬、沉砂池容量依設計（示意值）。
4. 沉砂池定期清淤並記錄；放流前符合放流水標準。
5. 洗車台至主要道路之車行路徑應鋪設：空污辦法 第8條【已核】

洗車台及沉砂池 平面圖

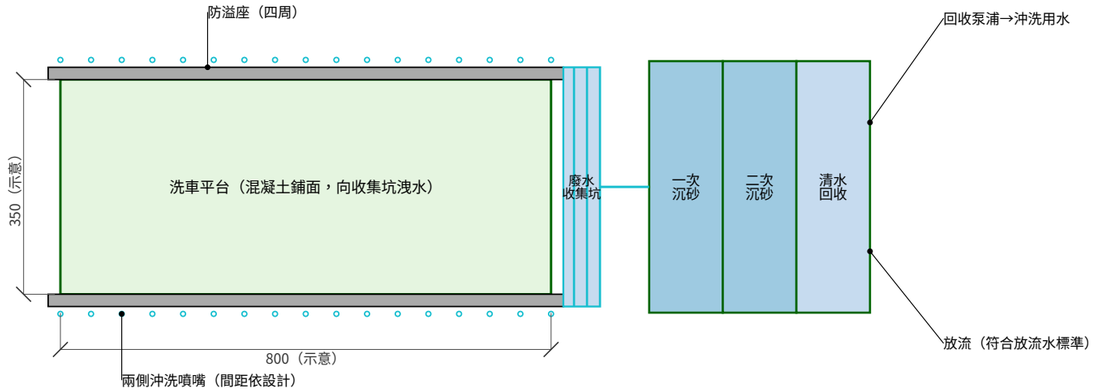

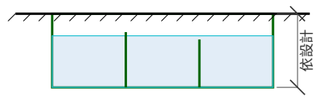

沉砂池斷面（溢流隔牆）

0　1　2　3　4 m


【已核】網路條文核對【待核】使用者核對
【地方】地方規定【示意】非法規值、依設計

審查

校核

繪圖

設計

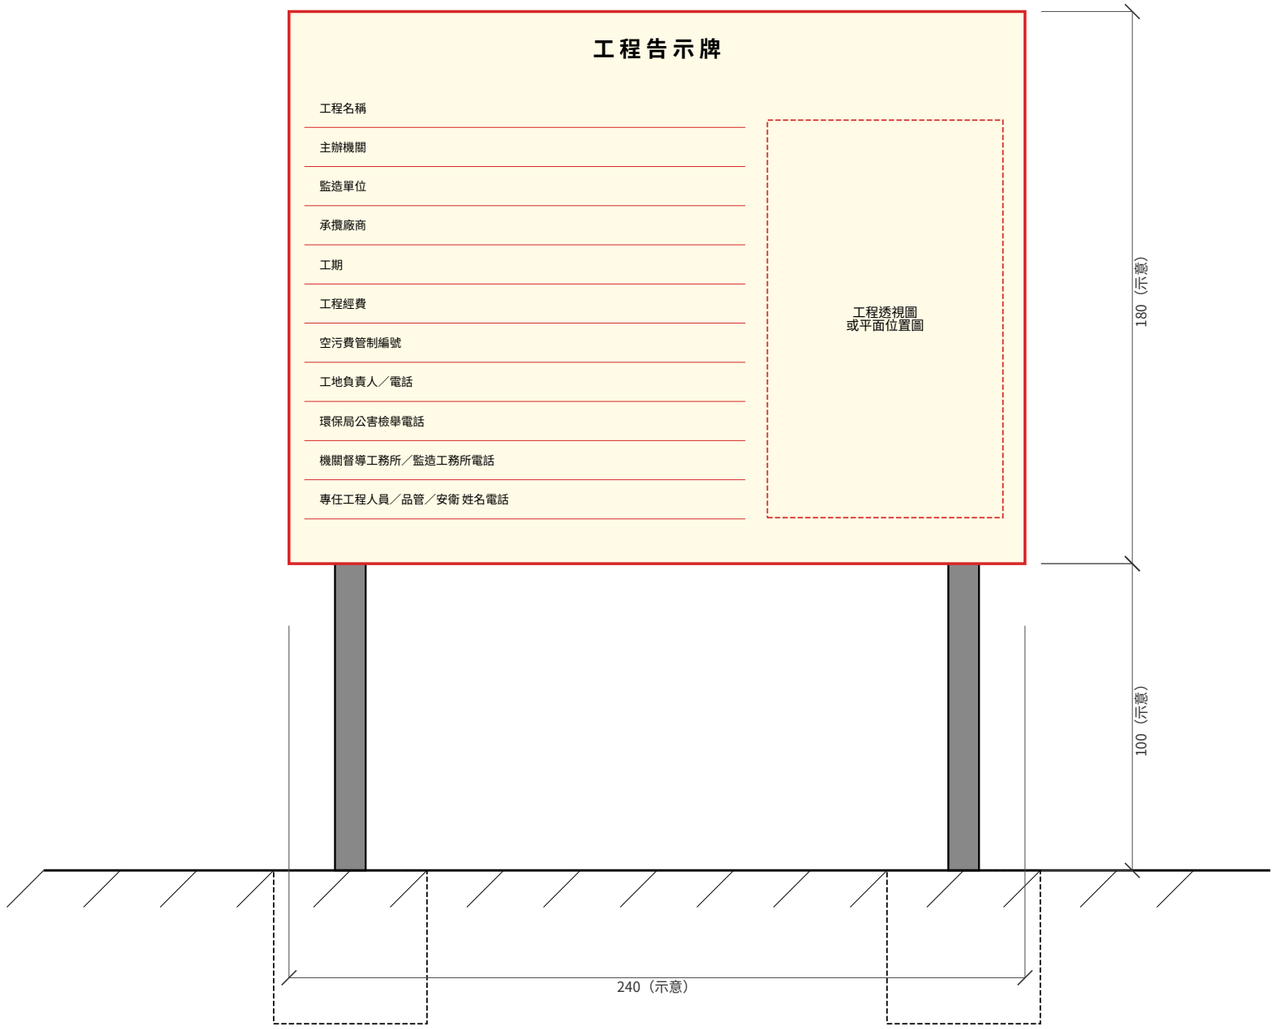

工程告示牌兼工地標示牌 立面圖

0 0.2 0.4 0.6 0.8 m

（工程名稱）

D04 工程告示牌詳圖

圖號：D04　比例：1:20（A3）

日期：2026-11-08　單位：公分（另註者除外）

附註

1. 工地標示牌應載明空污費管制編號、工地負責人姓名電話、環保局公害檢舉電話：空污辦法 第5條【已核】
2. 查核金額以上工程增列督導及監造工務所電話、專任工程人員、品管、安衛人員姓名電話、透視圖或平面位置圖：綱要規範 01581 3.1 .6（營建署版）【已核】
3. 告示牌尺寸、材料、字體依契約圖說（示意值）；設於主要出入口明顯處。
4. 臺北市開挖面積 3000 m² 以上且多面臨路者，每一鄰向距出入口每 50 m 增設：北市方案 二(五)【地方】
5. 竣工驗收合格前拆除，或經工程司同意後拆除。

【已核】網路條文核對【待核】使用者核對
【地方】地方規定【示意】非法規值、依設計


審查

校核

繪圖

設計

施工構台 縱斷面圖

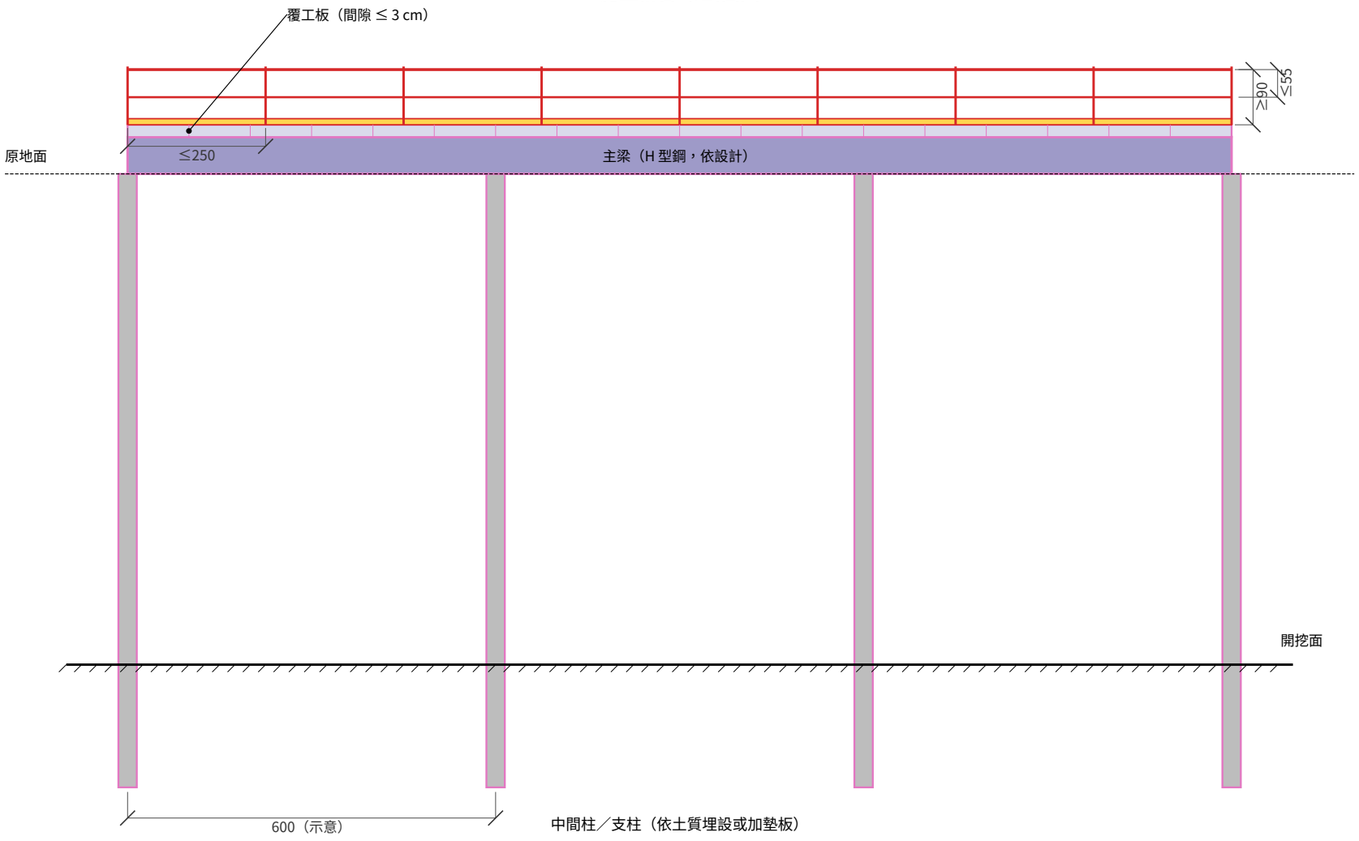

0 1 2 3 4 m

（工程名稱）

D05 施工構台詳圖

圖號：D05　比例：1:100（A3）

日期：2026-11-08　單位：公分（另註者除外）

附註

1. 施工構台須依結構力學設計，備施工圖說及強度計算書並簽章，建立依圖施工查驗機制：營造標準 第40條【已核】
2. 覆工板間隙 ≤ 3 cm；支柱依土質埋設或加墊板，連接部位以螺栓或鉚釘固定：營造標準 第62條之1【已核】
3. 構台寬度足供機具運轉，並預留起重機外伸撐座與材料堆置場地；載重標示牌設於明顯處。
4. 構台邊緣設護欄：上欄杆 ≥ 90 cm、開口 ≤ 55 cm、腳趾板：營造標準 第20條【已核】
5. 跨距、支柱間距、梁型號與構台高度均依設計（示意值）。

【已核】網路條文核對【待核】使用者核對
【地方】地方規定【示意】非法規值、依設計

審查

校核

繪圖

設計

（工程名稱）

D06 出土坡道詳圖


圖號：D06　比例：1:250（A3）

日期：2026-11-08　單位：公分（另註者除外）


附註

1. 坡度、寬度、轉彎半徑與鋪面依最大出土車輛性能設計（示意值，非法規值）。
2. 自設道路坡度不得使車輛機械有滑下可能；邊緣及開口設防止翻落設施：設施規則 第118條第6款【已核】
3. 坡道兩側高差 2 m 以上設護欄（上欄杆 ≥ 90 cm）：營造標準第19條【已核】
4. 單行坡道寬 ≥ 車寬＋1 m，雙向 ≥ 2×車寬＋1 m：設施規則通道章（條號待核）【待核】
5. 坡道鋪面計入車行路徑鋪設比例；坡底設集水坑抽排。

出土坡道 縱斷面圖

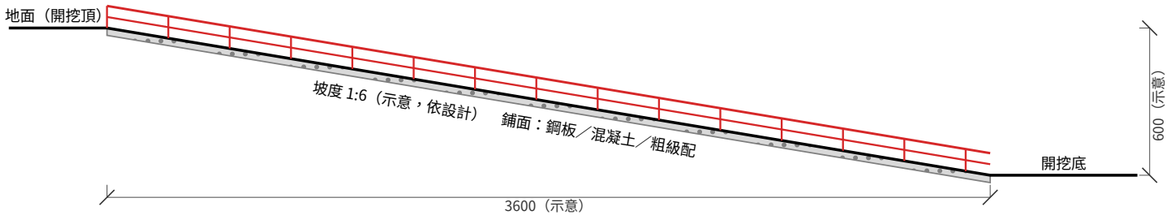

橫斷面圖

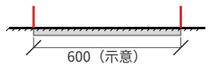



【已核】網路條文核對【待核】使用者核對
【地方】地方規定【示意】非法規值、依設計

審查	
校核	
繪圖	
設計	

（工程名稱）


D07 開挖周邊護欄及擋土詳圖

圖號：D07　比例：1:100（A3）

日期：2026-11-08　單位：公分（另註者除外）

附註

1. 開挖深 1.5 m 以上且有勞工進入，應設擋土支撐：營造標準 第71條【已核】
2. 擋土支撐依地質資料設計、繪製詳細圖樣並由專任工程人員或執業技師簽章（營造標準第73條）【已核】
3. 開挖出之土石不得堆積於開挖面上方；與開挖面高度等值之坡肩寬度範圍：營造標準 露天開挖章（條號待核）【待核】
4. 開挖周邊高差 2 m 以上設護欄：營造標準 第19條【已核】
5. 護欄前 2 m 內不得堆放物料、停放機械：營造標準 第20條【已核】
6. 周邊設截水溝防止地表水流入；設安全上下設備（樓梯塔）。
7. 基坑周邊加工場、堆載及構台荷重須經擋土設計者確認。

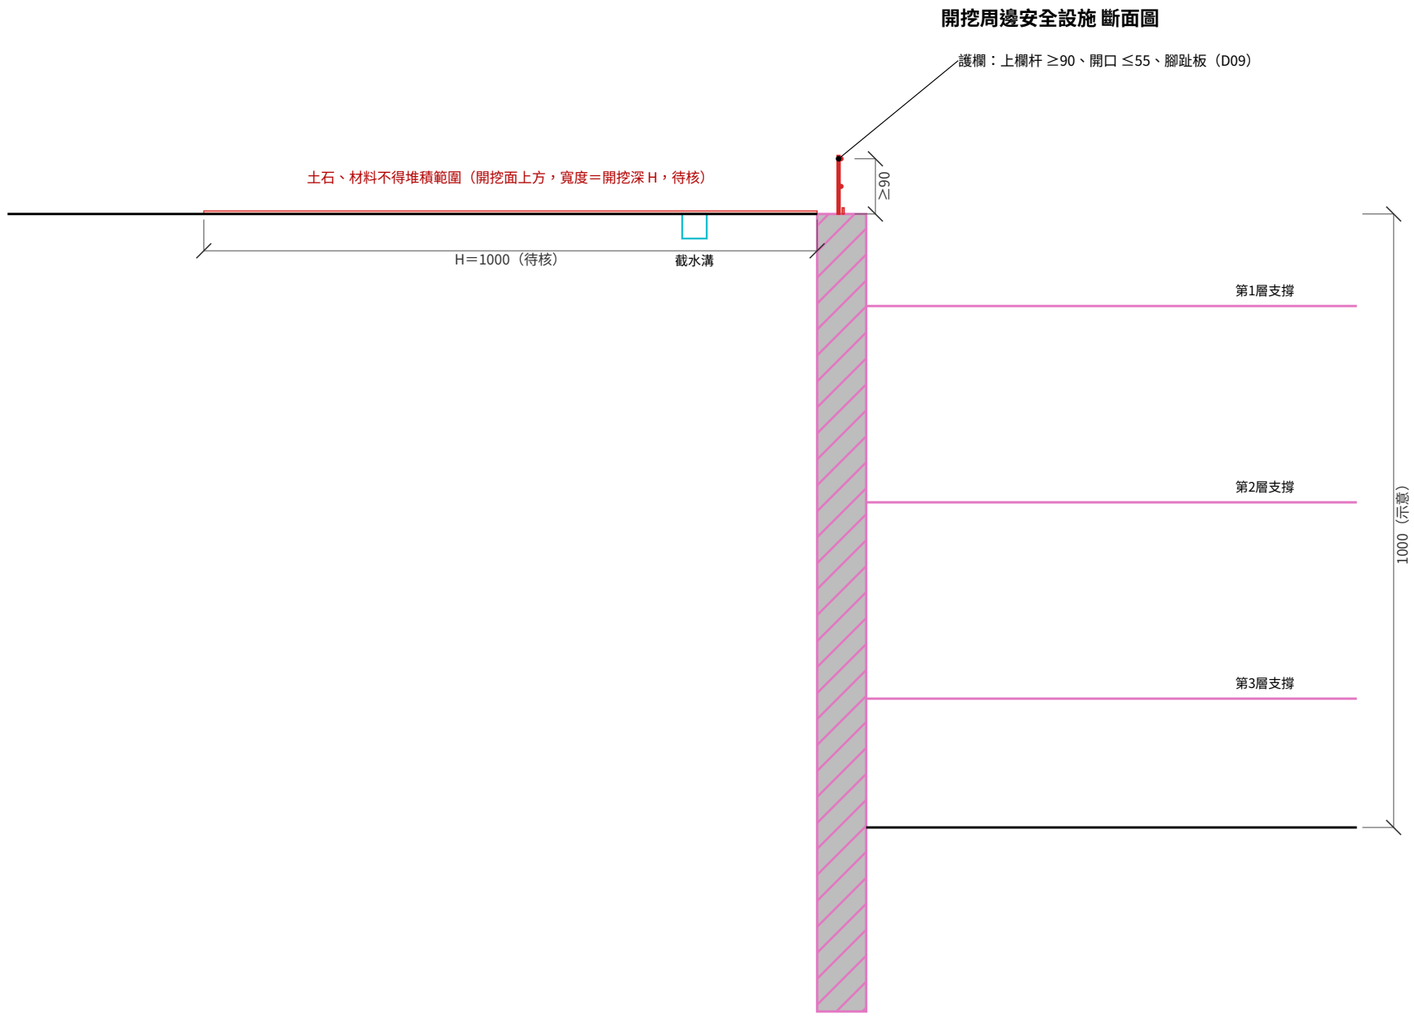

擋土壁（型式依設計）

0　1　2　3　4 m

【已核】網路條文核對【待核】使用者核對
【地方】地方規定【示意】非法規值、依設計

審查

校核

繪圖

設計

（工程名稱）

D08 施工架及安全網詳圖


圖號：D08　比例：1:100（A3）

日期：2026-11-08　單位：公分（另註者除外）


附註

1. 連接間距 垂直 ≤ 5.5 m、水平 ≤ 7.5 m：營造標準 第45條【已核】
2. 工作臺寬 ≥ 40 cm，踏板縫 ≤ 3 cm，低於立柱頂 ≥ 1 m：營造標準 第48條【已核】
3. 施工架與構造物間隙 ≤ 20 cm（超過設補助板料或安全網）：勞動檢查機構框式施工架作業安全指引 職安署／高雄市勞檢處指引【已核】
4. 高 ≥ 7 m 且立面 ≥ 330 m² 須設計簽章：營造標準 第40條【已核】；高 ≥ 5 m 指派作業主管：營造標準 第41條【已核】
5. 安全網攔截高度 ≤ 7 m，符合 CNS 14252／16079：營造標準 第22條【已核】；外伸寬度：營造標準 第22條【待核】
6. 結構體施工架外緣覆蓋防塵網或防塵布：空污辦法 第11條【已核】
7. 兩端立架、轉角及上下設備處設護欄；設安全上下設備。
8. 架高、跨距、層高依設計（示意 15 m × 15 m）。

框式施工架 立面圖（外覆防塵網）

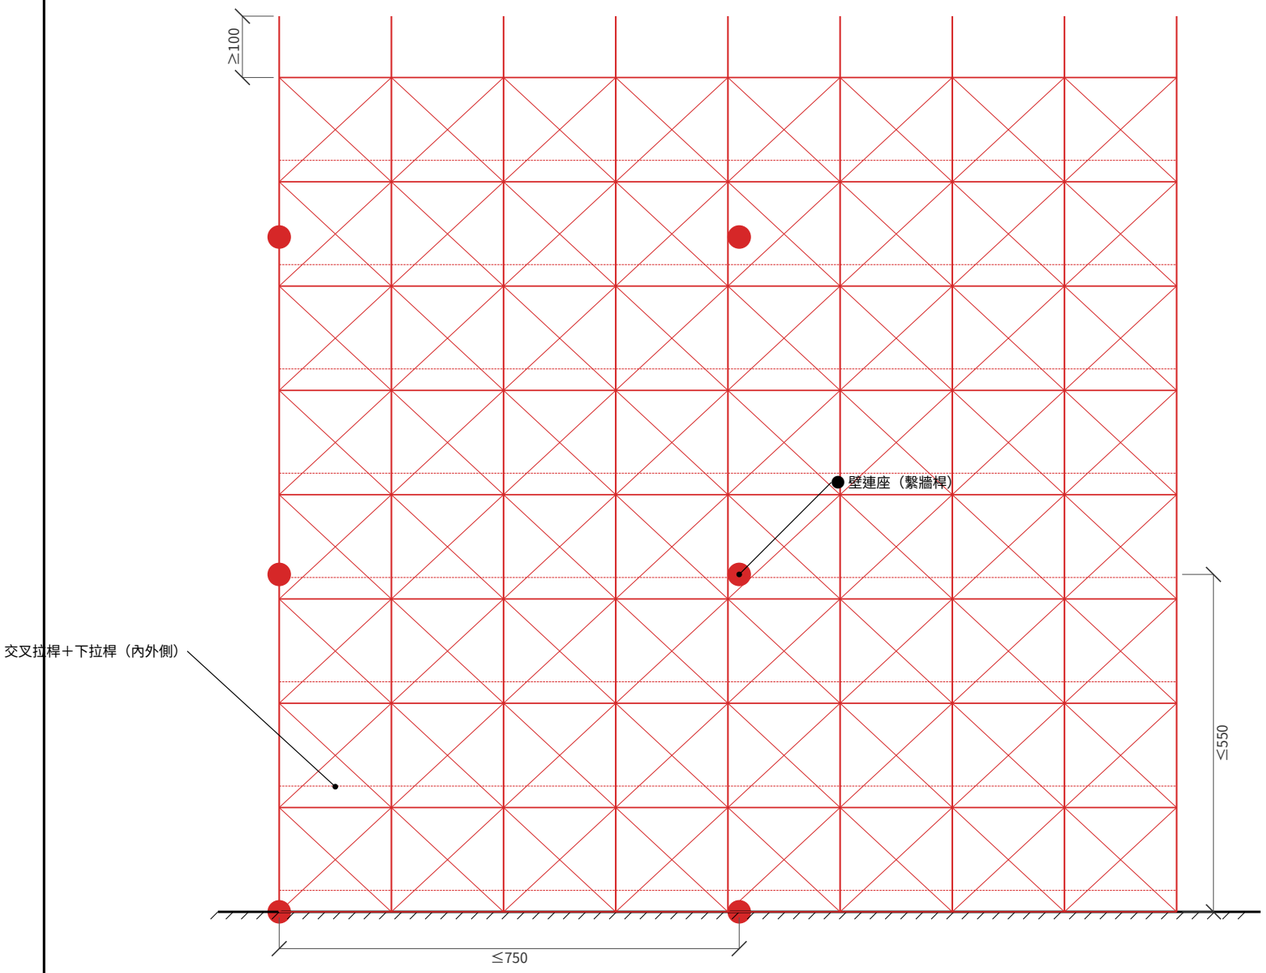

斷面圖

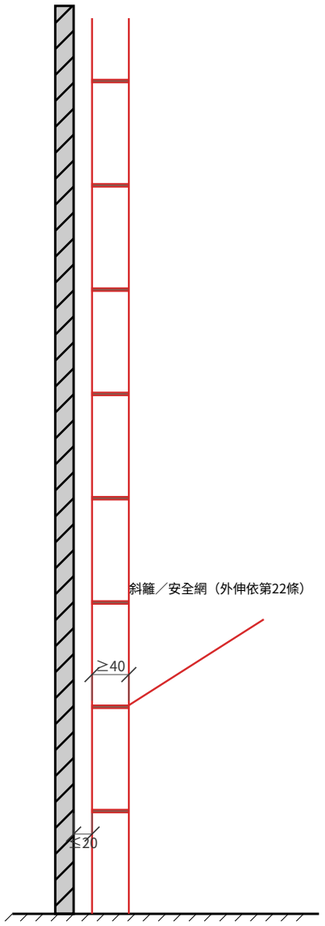

0　1　2　3　4 m


【已核】網路條文核對【待核】使用者核對
【地方】地方規定【示意】非法規值、依設計

審查


校核

繪圖

設計

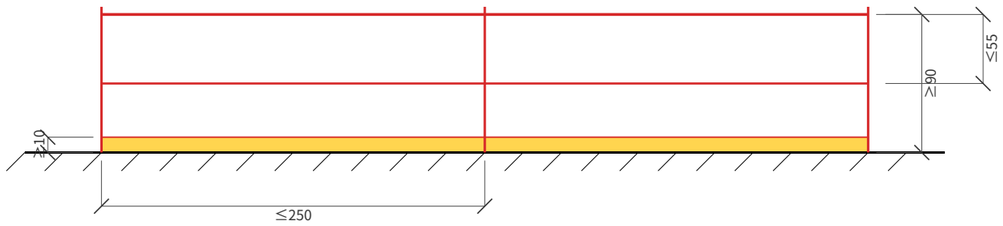

鋼管護欄 立面圖

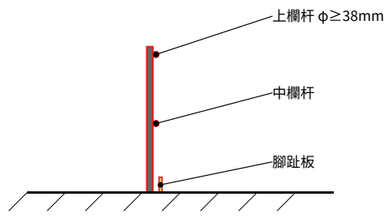

斷面圖

0 0.5 1 1.5 2 m

（工程名稱）

D09 護欄標準詳圖

圖號：D09　比例：1:40（A3）

日期：2026-11-08　單位：公分（另註者除外）

附註

1. 上欄杆高 ≥ 90 cm；上、中欄杆與樓板間開口 ≤ 55 cm：營造標準 第20條【已核】
2. 腳趾板高 ≥ 10 cm：營造標準 第20條【待核】
3. 鋼管欄杆及杆柱直徑 ≥ 38 mm；杆柱間距 ≤ 2.5 m：營造標準 第20條【已核】
4. 上欄杆任一點任何方向承受 75 kgf 無顯著變形：營造標準 第20條【已核】
5. 護欄前方 2 m 內不得堆放物料、停放機械或使用梯凳：營造標準 第20條【已核】
6. 適用處所：高度 2 m 以上之開口、樓梯、坡道、工作臺、擋土設施、構臺邊緣等：營造標準 第19條【已核】

【已核】網路條文核對 【待核】使用者核對
【地方】地方規定 【示意】非法規值、依設計

審查

校核

繪圖

設計

（工程名稱）

D10 開口護蓋詳圖


圖號：D10　比例：1:25（A3）

日期：2026-11-08　單位：公分（另註者除外）


附註

1. 護蓋具承受人員、車輛通過之強度；供車輛通行者以後軸載重 2 倍設計：營造標準 第21條【已核】
2. 柵狀護蓋間隔 ≤ 3 cm；臨時開口護蓋漆黃色並標示警告：營造標準 第21條【已核】
3. 護蓋固定防止滑動、掉落或移位；上方不得放置超過設計強度之重物。
4. 高度 2 m 以上之開口應設護欄、護蓋或安全網：營造標準 第19條【已核】
5. 護蓋板厚與擋塊尺寸依開口尺寸及荷重設計（示意）。

開口護蓋 平面圖

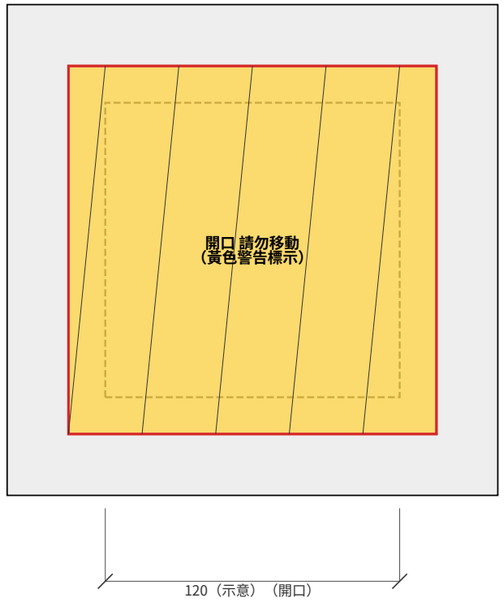

斷面圖

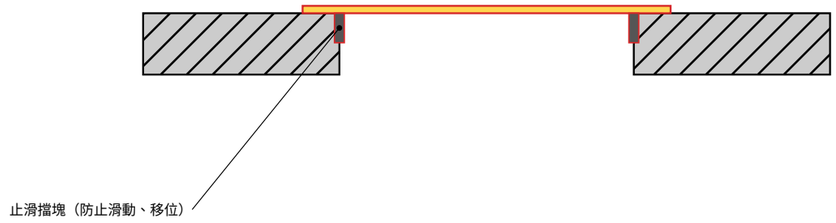


0　0.2　0.4　0.6　0.8 m

【已核】網路修文核對【待核】使用者核對
【地方】地方規定【示意】非法規值、依設計

審查	
校核	
繪圖	
設計	

臨時用電系統單線圖（不依比例）

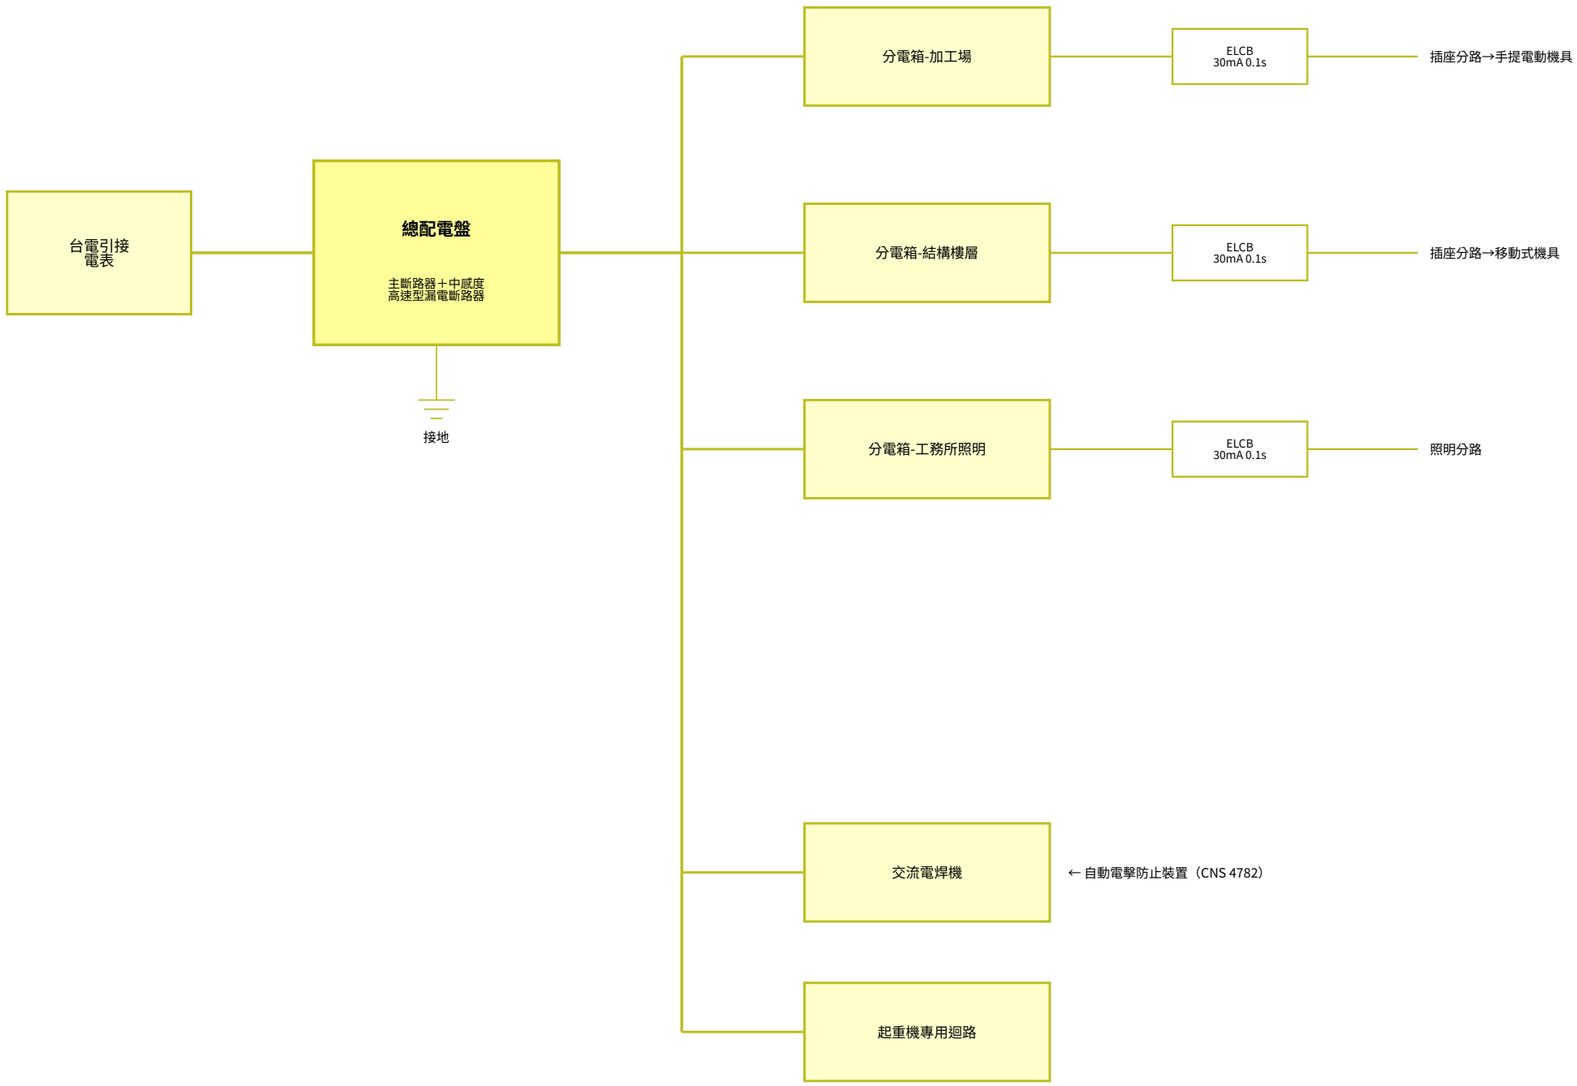

（工程名稱）

D11 臨時用電系統詳圖

圖號：D11　比例：NTS 不依比例（A3）

日期：2026-11-08　單位：公分（另註者除外）


附註

1. 移動式或攜帶式電動機具（對地 150 V 以上、潮濕場所、鋼架上等）連接電路設高敏感度高速型漏電斷路器 30 mA、0.1 s 以內：設施規則 第243條【已核】
2. 建築或工程興建之臨時用電，外殼接地電阻符合時得用中感度高速型（50～1000 mA）：設施規則 第243條；屋內線路裝置規則第59條【已核】
3. 交流電焊機於良導體狹小空間或鋼架上作業設自動電擊防止裝置：設施規則 第250條【已核】
4. 漏電斷路器以設於分路為原則；配電箱加鎖、防雨、張貼負責人與檢點紀錄。
5. 電纜架高或穿管保護，不得置於車行路徑地面；分路數與容量由合格電機人員設計。
6. 起重機作業半徑內之架空電線須洽電業單位防護或遷移。

【已核】網路條文核對 【待核】使用者核對
【地方】地方規定 【示意】非法規值、依設計


審查	
校核	
繪圖	
設計	

截水導水系統 平面示意圖

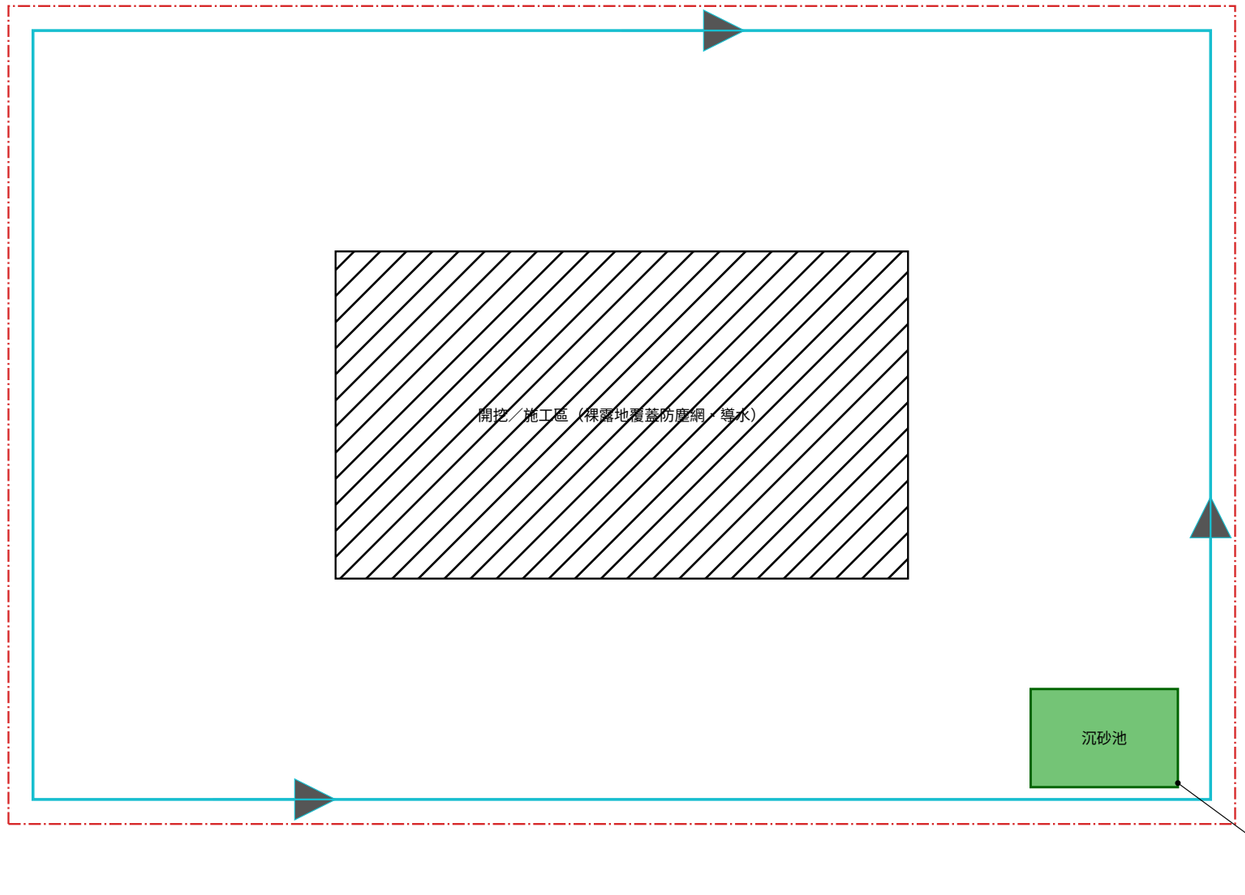

0 2 4 6 8 m

截水溝斷面

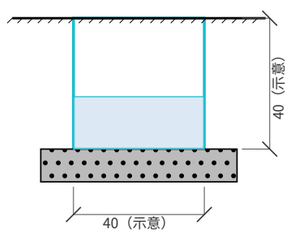

（斷面放大 8 倍繪製）

（工程名稱）

D12 截水溝及沉砂池詳圖

圖號：D12　比例：1:150（A3）

日期：2026-11-08　單位：公分（另註者除外）

附註

1. 營建工地逕流廢水污染削減計畫施工前報核；圖面標示遮雨、擋雨、導雨設施及沉砂池：水措辦法 第10條【已核】
2. 遮雨：帆布覆蓋或開挖面鋪設；擋雨：擋水牆、砂包；導雨：排水溝或臨時土溝（地方環保局宣導資料）。
3. 裸露區域採行防制措施面積比例：第一級 ≥ 90%、第二級 ≥ 70 %：空污辦法 第9條【已核】
4. 截水溝斷面、坡度與沉砂池容量依集水面積與降雨強度設計（示意值）。
5. 沉砂池定期清淤；颱風豪雨前加強檢查。

【已核】網路條文核對【待核】使用者核對
【地方】地方規定【示意】非法規值、依設計


審查

校核

繪圖

設計

工務所 平面圖（組合屋／貨櫃屋單元）

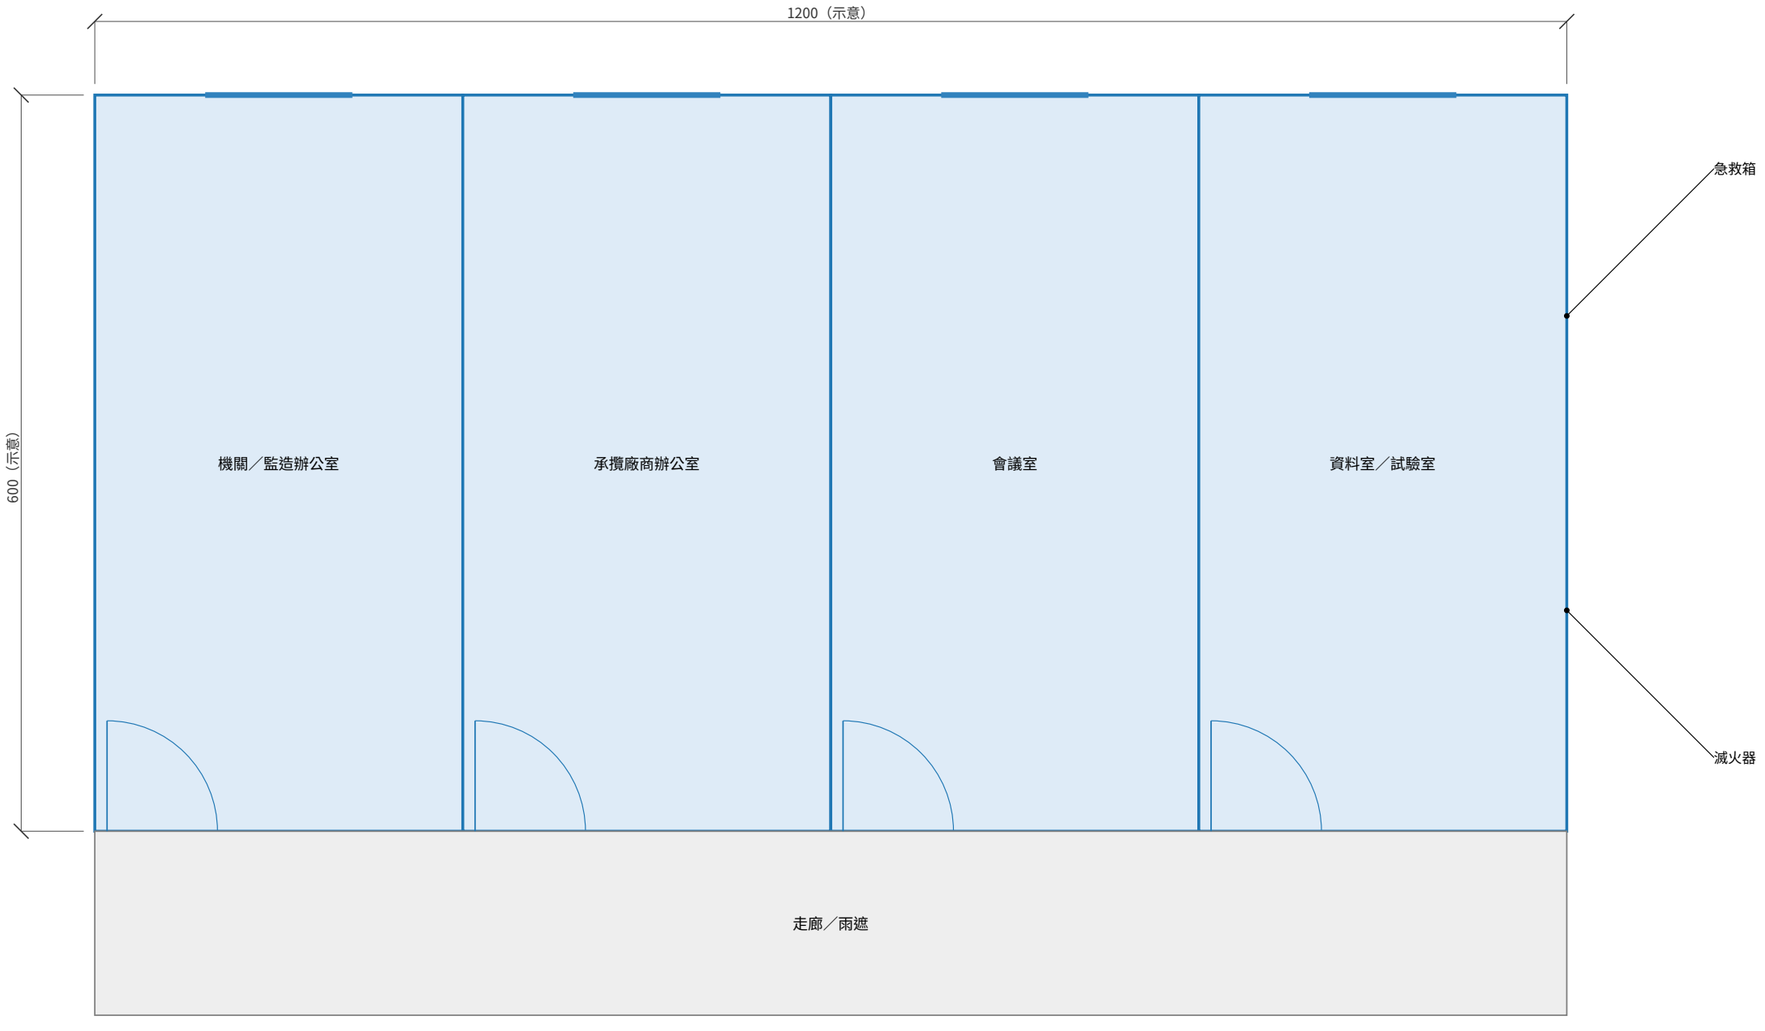

0　0.5　1　1.5　2 m

（工程名稱）

D13 工務所詳圖

圖號：D13　比例：1:50（A3）

日期：2026-11-08　單位：公分（另註者除外）

附註

1. 工務所位置避開起重機作業半徑、開挖影響範圍與主要車行動線。
2. 房間組成、單元尺寸依契約（01500、01510 臨時房舍及監工站；示意值）。
3. 電源由分電箱引接並設漏電斷路器；設滅火器、急救箱與緊急聯絡資訊。
4. 高氣溫戶外作業者，休息場所設置依設施規則（113.08.01 修正）辦理。
5. 基礎墊高、防颱繫固依設計；二層以上組合屋須檢核結構與樓梯。

【已核】網路條文核對【待核】使用者核對
【地方】地方規定【示意】非法規值、依設計


審查

校核

繪圖

設計

男女廁所浴室 平面圖（同時作業 男 50／女 5 人）

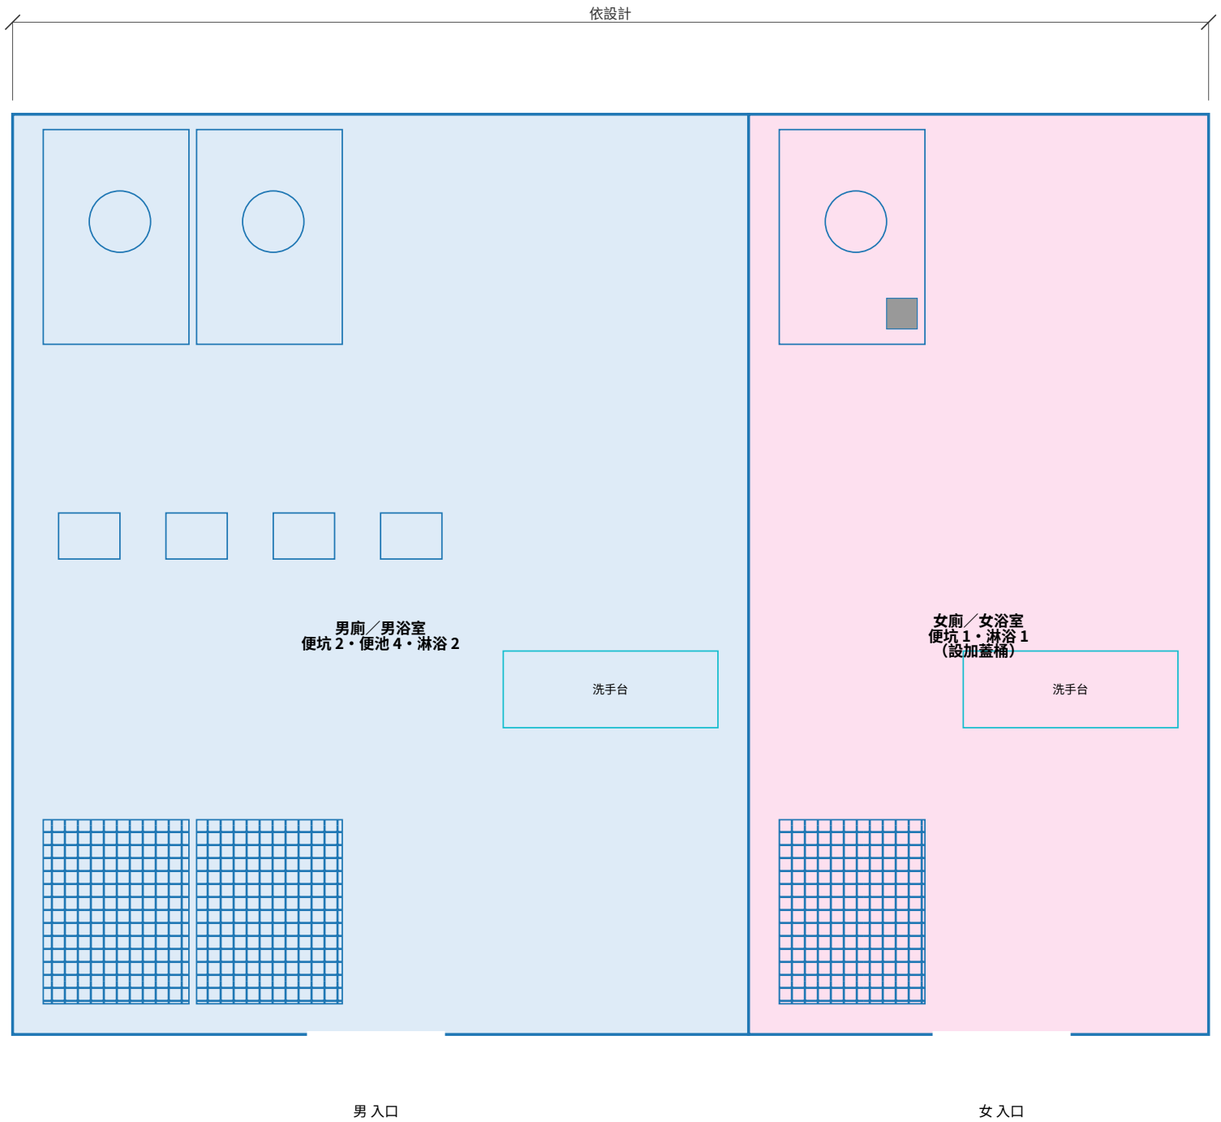

0　0.5　1　1.5　2 m

（工程名稱）

D14 男女廁所及浴室詳圖

圖號：D14　比例：1:40（A3）

日期：2026-11-08　單位：公分（另註者除外）

附註

1. 男用便坑每 25 人 1 個（最少每 60 人 1 個）：設施規則 衛生章（條號待核）【待核】
2. 男用便池每 15 人 1 個：設施規則 衛生章（條號待核）【待核】
3. 女用便坑每 15 人 1 個；女廁設加蓋桶：設施規則 衛生章（條號待核）【待核】
4. 男女廁所分別設置、入口分開並明顯標示；設充分供應清潔水質之洗手設備。
5. 淋浴間數量非法規值（示意：男每 25 人 1 間），依契約或工程需要調整。
6. 污水接化糞池或專用槽並定期抽除，不得排入雨水溝；流動廁所可計入便器數。

【已核】網路條文核對【待核】使用者核對
【地方】地方規定【示意】非法規值、依設計

審查

校核

繪圖

設計

（工程名稱）

D15 材料堆置場詳圖

圖號：D15　比例：1:100（A3）

日期：2026-11-08　單位：公分（另註者除外）

附註

1. 粉塵逸散性材料（砂石、土方、廢棄物）覆蓋防塵布、防塵網或噴灑化學穩定劑：空污辦法 第7條【已核】
2. 護欄前 2 m 內不得堆放物料：營造標準 第20條【已核】
3. 開挖面上方不得堆積土石，距開挖邊緣淨距 ≥ 開挖深 H：營造標準 露天開挖章（條號待核）【待核】
4. 搬運通道寬度：設施規則 通道章（條號待核）【待核】
5. 建築材料、機具及廢棄物堆放於安全圍籬內：北市方案 三【地方】
6. 堆置高度、墊木間距、分區面積依材料數量與吊運方式設計（示意值）；基坑周邊堆載經擋土設計者確認。



0　1　2　3　4 m

【已核】網路條文核對【待核】使用者核對
【地方】地方規定【示意】非法規值、依設計

審查	
校核	
繪圖	
設計	